



BẢNG PHÂN BỐ PN

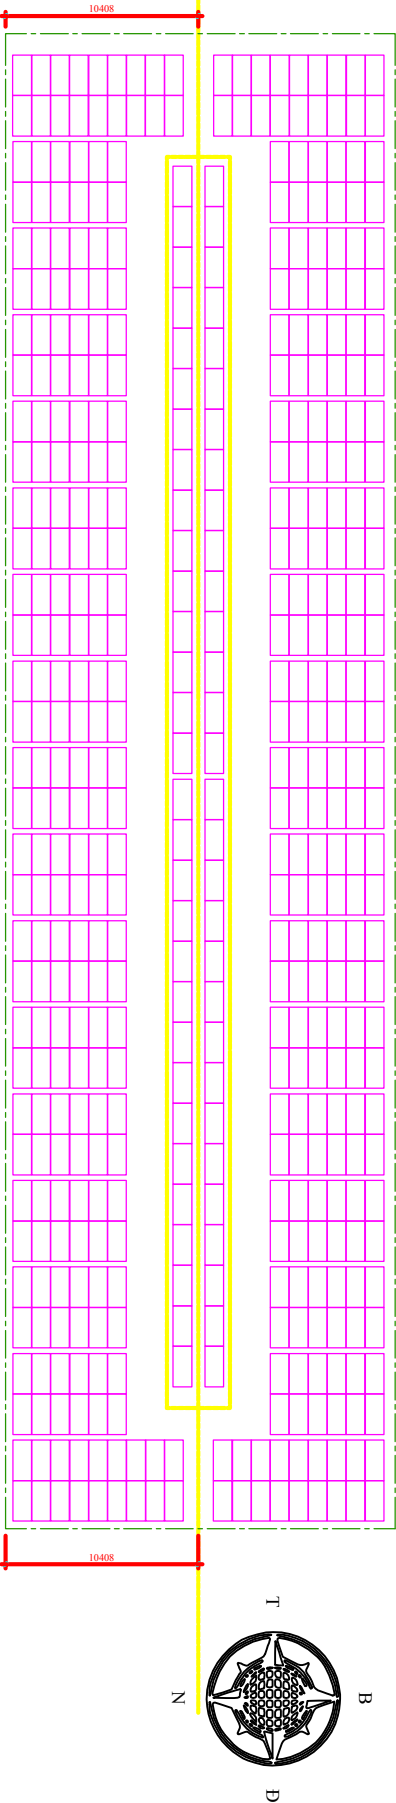

BẢNG PHÂN BỐ INVERTER

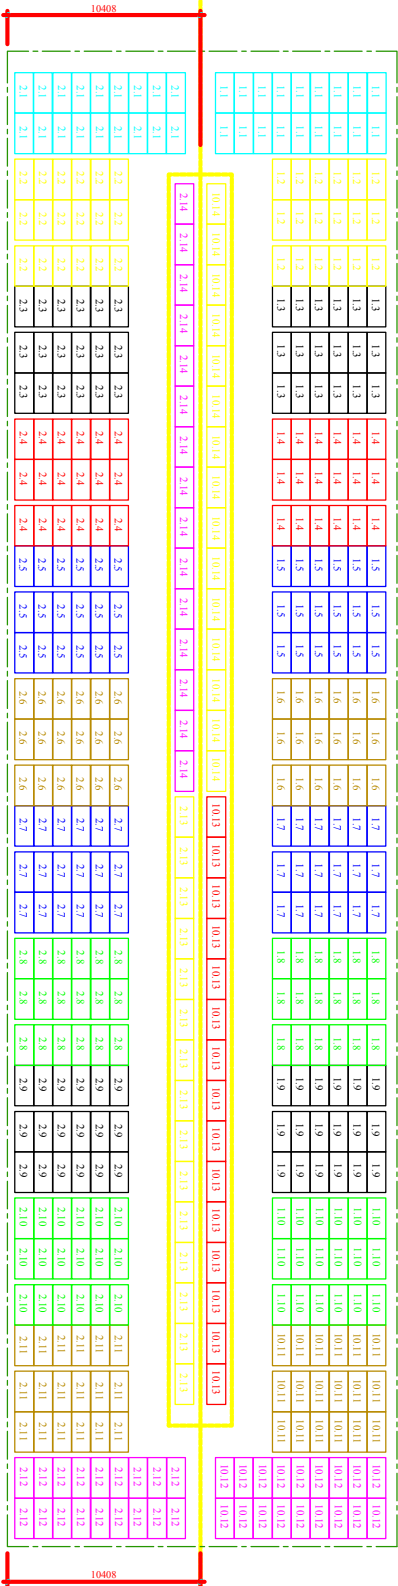

CHI TIẾT DÂY DẪN

SUN2000-100KTL-M1					INV5: SN: ES2050003147				
MPPT1	MPPT2	MPPT3	MPPT4	MPPT5	MPPT6	MPPT7	MPPT8	MPPT9	MPPT10
PV1	PV3	PV5	PV7	PV9	PV11	PV13	PV15	PV17	PV19
PV2	PV4	PV6	PV8	PV10	PV12	PV14	PV16	PV18	PV20
18	18	18	18	18	18	15	...	...	...
18	18	18	18	18	18	15	...	...	...
1.1	1.3	1.5	1.7	1.9	1.11	1.13	...	...	...
1.2	1.4	1.6	1.8	1.10	1.12	1.14	...	...	...

SUN2000-100KTL-M1					INV5: SN: ES2050003147				
MPPT1	MPPT2	MPPT3	MPPT4	MPPT5	MPPT6	MPPT7	MPPT8	MPPT9	MPPT10
PV1	PV3	PV5	PV7	PV9	PV11	PV13	PV15	PV17	PV19
PV2	PV4	PV6	PV8	PV10	PV12	PV14	PV16	PV18	PV20
18	18	18	18	18	18	15	...	...	...
18	18	18	18	18	18	15	...	...	...
2.1	2.3	2.5	2.7	2.9	2.11	2.13	...	...	...
2.2	2.4	2.6	2.8	2.10	2.12	2.14	...	...	...

- TỔNG CÔNG SUẤT: 221.400KWP Pn-450wp
- TỔNG SỐ INV: 02.100kwp
- HỆ SỐ QUẢ TÀI MBA: 18.8%
- HỆ SỐ QUẢ TÀI INV: 5.6%



D

STT	NGÀY	NỘI DUNG	DUYỆT
NO	DATE	DESCRIPTION	APPROVAL
1			
2			
3			

TÊN DỰ ÁN PROJECT NAME

NĂNG LƯỢNG MẶT TRỜI
ÁP MẠI

ĐC: Xã Thanh Hòa, huyện Ba Đồn,
tỉnh Bình Phước

CHỦ ĐẦU TƯ OWNER

CƠ SỞ CHẾ BIẾN HẠT BIỂU
A. BÌ

ĐC: Xã Thanh Hòa, huyện Ba Đồn,
tỉnh Bình Phước

ĐƠN VỊ THI CÔNG

HỆ THỐNG
MINH THỊNH

CÔNG TY TNHH HIỆP
MINH THỊNH

ĐC: TT THANH BÌNH, HUYỆN BÀ ĐỒN, TỈNH BÌNH PHƯỚC
ĐT: 08663.6867
EMAIL: HIEP@HIEPNGHIA.COM

GIAO DẪN

TRƯỜNG CÔNG TRÌNH

CHỦ TRÌ

HIỆP MINH THỊNH

QUẢN LÝ KỸ THUẬT

NGƯỜI CHỨC DUYỆT

GIAO SỬ THỰC CÔNG

GIAO ĐOÀN

BẢN VẼ THIẾT KẾ

HẠNG MỨC CÔNG TRÌNH

TÊN BẢN VẼ DRAWING TITLE

MẶT BẰNG TỔNG THỂ
LẬP PHN NĂNG LƯỢNG MẶT TRỜI

TỶ LỆ NGÀY HOÀN THÀNH
SCALE DATE

2020 KC - 00