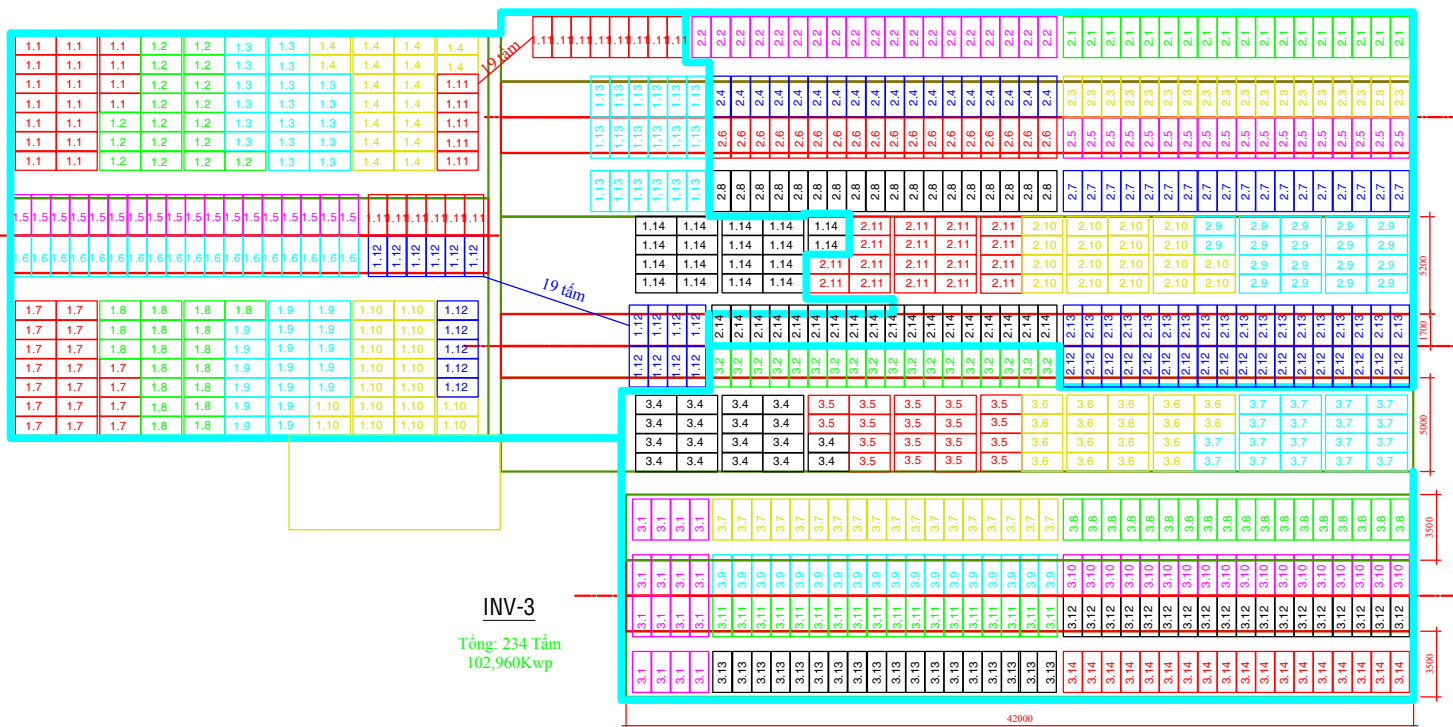


INV-1

NHÀ A: 253 Tầm
111,32Kwp

INV-2

Tổng cộng: 254 Tầm
111,320KwpTổng cộng : INV1+INV2+INV3= 741Tầm
326,040Kwp

INV-1

INV1-SUN2000-100KTL-M1

10-MPPT-20 INPUT

18 18 18 18 18 18 19 19
18 18 18 18 18 18253 tấm pin:
111,32kWP

INV-2

INV1-SUN2000-100KTL-M1

10-MPPT-20 INPUT

18 18 18 18 18 18 18 18
18 18 18 18 18 18253 tấm pin:
111,32kWP

INV-3

INV1-SUN2000-100KTL-M1

10-MPPT-20 INPUT

18 18 18 18 18 18 18 16
18 18 18 18 18 18250 tấm pin:
110kWPTổng cộng: 756 tấm
Power: 332,64kWPCÔNG TY TNHH TƯ VẤN THIẾT KẾ
HOÀNG ANCÔNG TRÌNH: XÂY DỰNG HỆ THỐNG NLMTAM 400KWP CTY TRỌNG ĐẠT ALPHA
ĐỊA ĐIỂM: TT THANH BÌNH - HUYỆN BÙ Đốp- TỈNH BÌNH PHƯỚC

MẶT BẰNG TỔNG THỂ GIAI ĐOẠN I

Giám đốc

Mai Ngọc Tiên

CNSA

Đào Ngọc Bình

VZ

Nguyễn Đức Hưng

T.K.K.T.C.T

Ngày

Tỉ lệ:

1/500000

MB_TT

Số BV

01

01