


PHÂN BỐ CÔNG SUẤT TRẠNG TRẠI THÂN BÙN
(PIN450WP)

INVERTER	C/S (WP)	STRING	SỐ TẤM
INV_01	126,000	18*8*450+6*16*450+2*20*450	280
INV_02	129,600	5*16*450+20*2*450+12*14*450	288
INV_03	124,200	16*16*450+20*450	276
INV_04	126,000	9*20*450+1*16*450+2*18*450+12*4*450	280
Tổng	505,800		1124

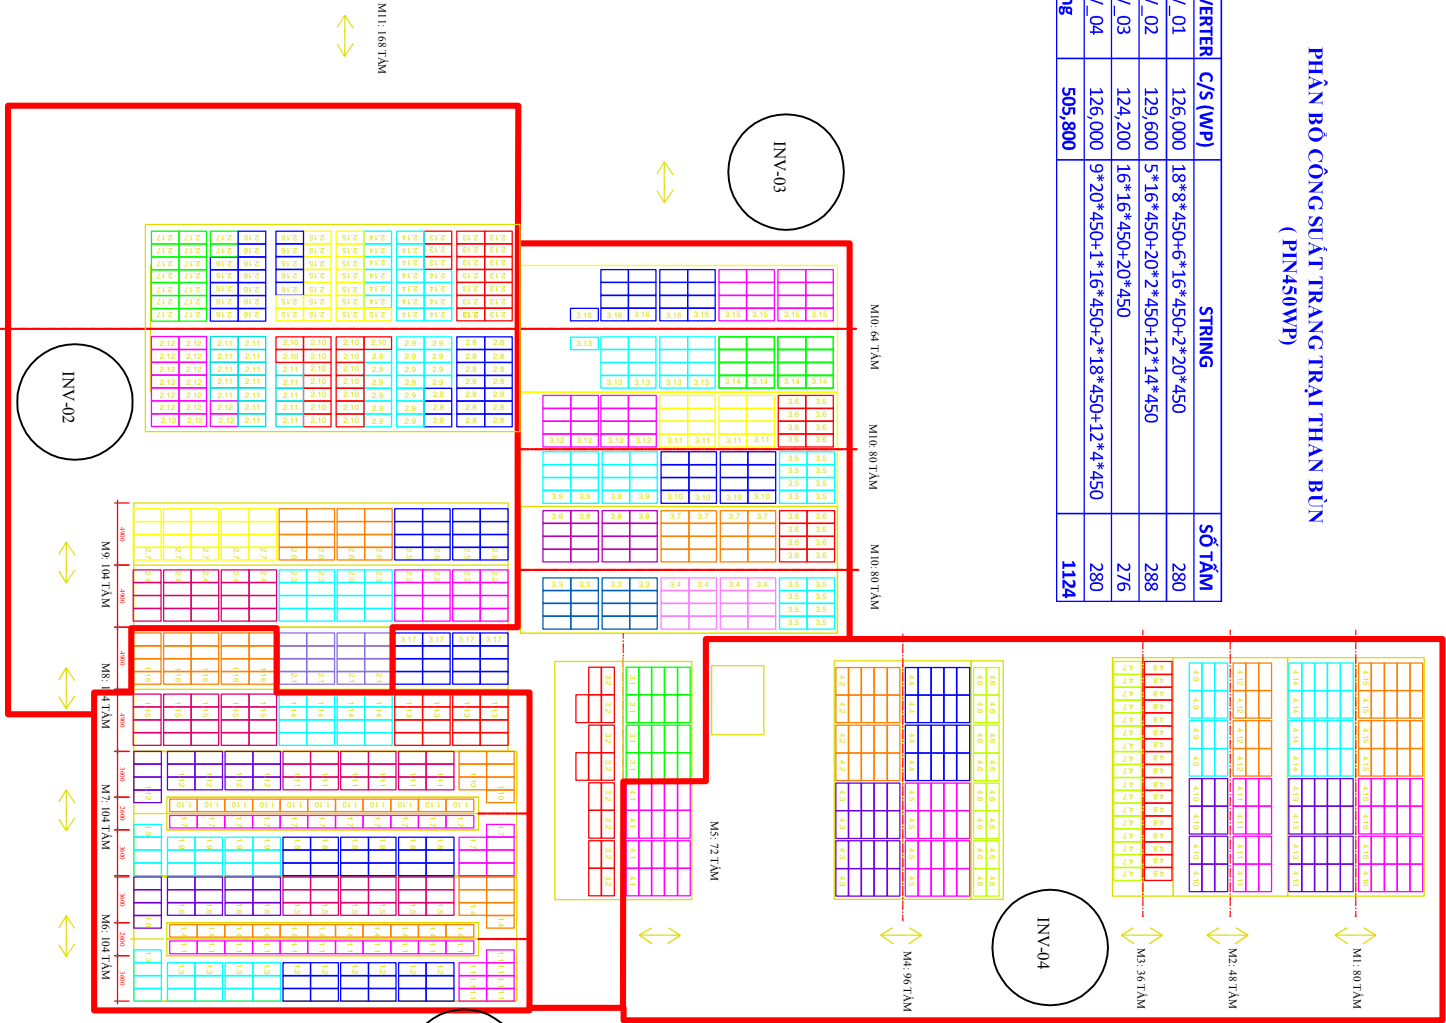

INVERTER 01

MPPT	PV STRING SỐ TẤM (450)
1	1 11 18
2	2 12 18
3	3 14 18
4	4 15 18
5	5 17 18
6	6 18 18
7	7 110 18
8	8 111 18
9	9 113 16
10	10 114 16
11	11 13 16
12	12 19 16
13	13 16 16
14	14 112 16
15	15 115 20
16	16 16 20
17	17 116 20
18	18 19 20
19	19 20 20
Tổng C/S	126,000

INVERTER 02

MPPT	PV STRING SỐ TẤM (450)
1	1 21 16
2	2 217 16
3	3 22 16
4	4 23 16
5	5 24 20
6	6 25 16
7	7 26 16
8	8 27 20
9	9 213 17
10	10 214 17
11	11 215 17
12	12 216 17
13	13 210 17
14	14 211 17
15	15 212 16
16	16 213 17
17	17 214 17
18	18 215 17
19	19 216 17
20	20 216 17
Tổng C/S	129,600

INVERTER 03

MPPT	PV STRING SỐ TẤM (450)
1	1 31 20
2	2 32 16
3	3 33 16
4	4 34 16
5	5 35 16
6	6 36 16
7	7 37 16
8	8 38 16
9	9 39 16
10	10 40 16
11	11 41 16
12	12 42 16
13	13 43 16
14	14 44 16
15	15 45 16
16	16 46 16
17	17 47 16
18	18 48 16
19	19 49 16
20	20 50 16
Tổng C/S	124,200

INVERTER 04

MPPT	PV STRING SỐ TẤM (450)
1	1 41 20
2	2 42 20
3	3 43 20
4	4 44 20
5	5 45 20
6	6 46 20
7	7 47 20
8	8 48 20
9	9 49 20
10	10 50 20
11	11 51 20
12	12 52 20
13	13 53 20
14	14 54 20
15	15 55 20
16	16 56 20
17	17 57 20
18	18 58 20
19	19 59 20
20	20 60 20
Tổng C/S	126,000

STT	NGÀY	NỘI DUNG	DUYỆT
NO	DATE	DESCRIPTION	APPROVAL
1			
2			
3			

TÊN DỰ ÁN PROJECT NAME

XÂY DỰNG HỆ THỐNG NHÀ MÁY
SOLAR WP CTY TNHH TM DV & XD
ĐIỆN KHƠI MINH

ĐC: Xã Tân Thành, H. Bù Đăng, T. Bình Phước

CHỦ ĐẦU TƯ OWNER

CTY TNHH TM DV & XD
ĐIỆN KHƠI MINH

ĐC: QUẬN THỦ ĐỨC - TP HCM

ĐƠN VỊ THI CÔNG

HỢP MINH THỊNH
SC&S

CTY TNHH HIỆP
MINH THỊNH

ĐC: TT THÂN BÌNH, HUYỆN BÚ ĐOP, TỈNH BÌNH PHƯỚC

ĐT: 086683887

EMAIL: HIEMINH@GMAIL.COM

GIAO ĐỐC

TRƯỜNG CÔNG TRÌNH

CHỈ TRỊ

ĐƠN VỊ CAO TỌA

QUẢN LÝ THIẾT

NGUYỄN DINH PH

NGƯỜI DẪN

ĐẠI LỊCH HỢP

GIAO SỬA THI CÔNG DD CHỦ ĐẦU TƯ

GIAO ĐỐC

ST&G

BẢN VẼ HOÀN CÔNG

HÀNG MỨC CÔNG TRÌNH

BUILDING IT

TÊN BẢN VẼ

BẢN VẼ MẶT BẰNG ĐẦU PİN

LẬP PİN NẰNG LƯỜNG MẶT TR

TÊN

SCALE

DATE

20/12/2020

KC - 00