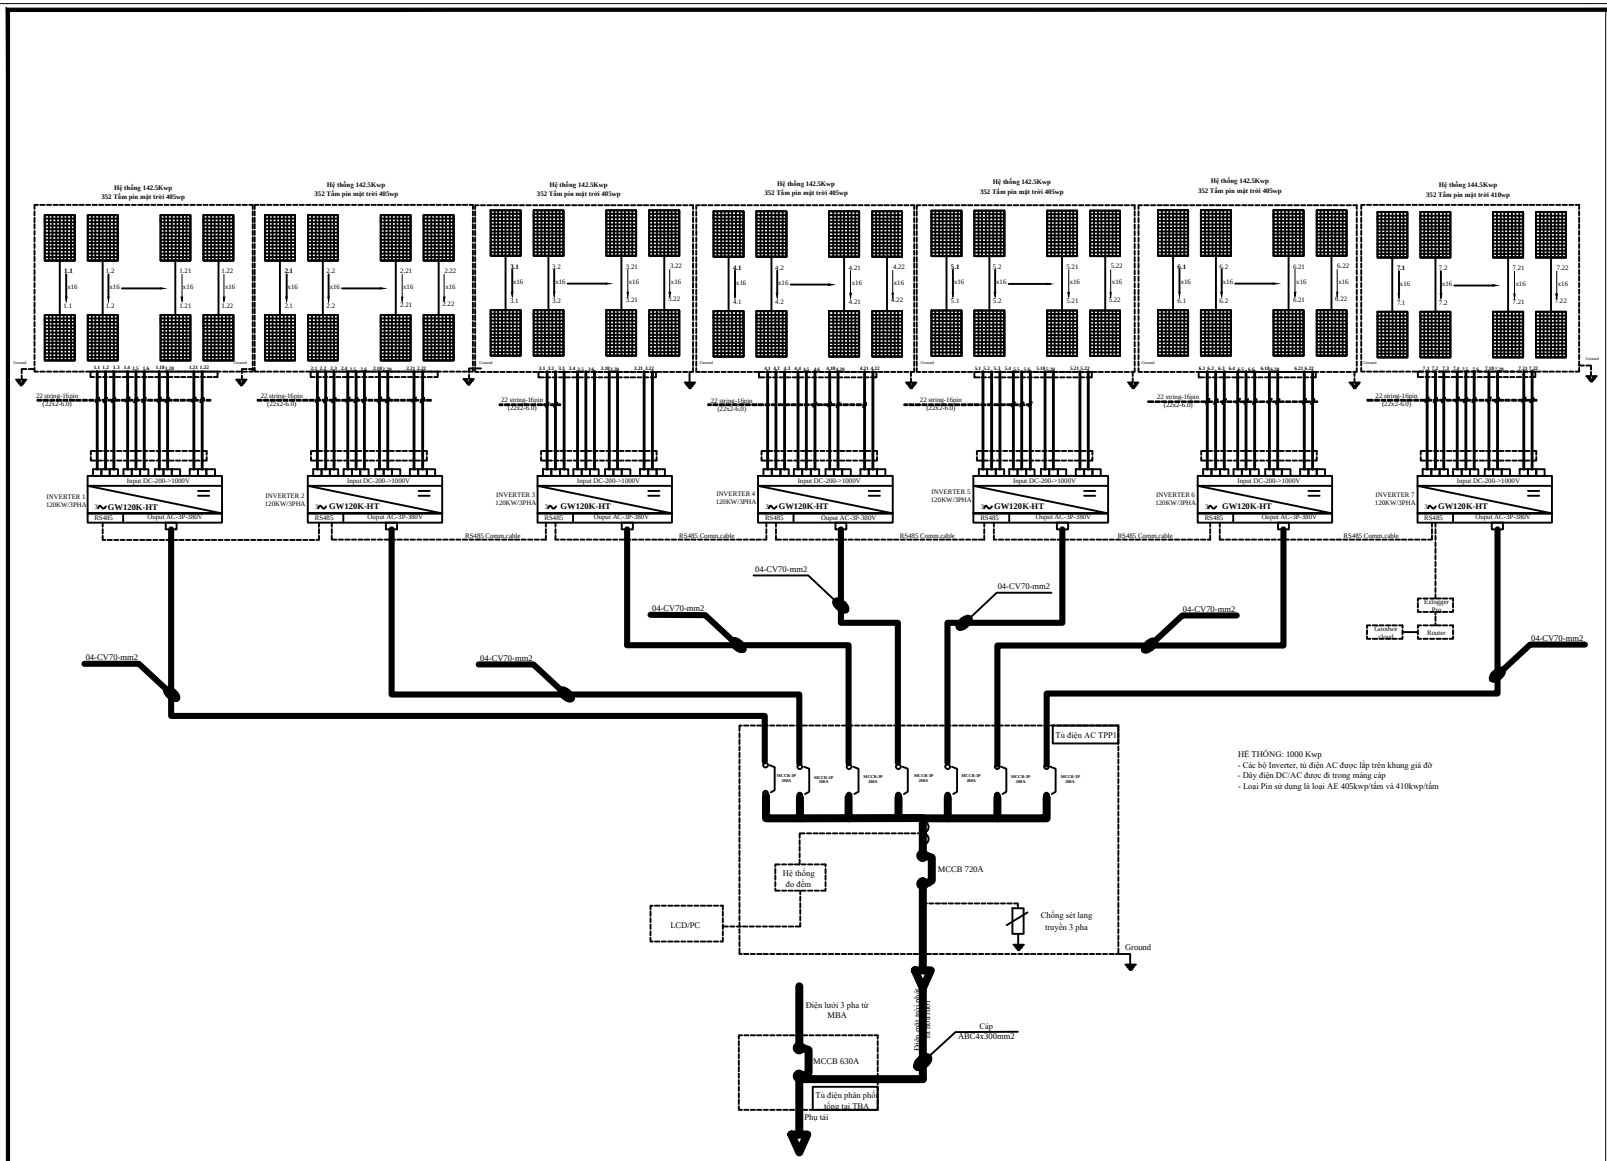



HIỆU CHỈNH REVISION

| STT NO | NGÀY DATE | NỘI DUNG DESCRIPTION | DUYỆT APPROVAL |
|---|---|---|---|
| 1 | | | |
| 2 | | | |
| 3 | | | |

TÊN DỰ ÁN PROJECT NAME

**XÂY DỰNG HỆ THỐNG NLMTAM 1000 KWP CTY TNHH NÔNG NGHIỆP NĂNG LƯỢNG HOÀNG VIÊN**

Đ/C: XÃ LONG BÌNH, HUYỆN PHÚ RIỀNG, TỈNH BÌNH PHƯỚC

CHỦ ĐẦU TƯ OWNER

**CÔNG TY TNHH NÔNG NGHIỆP NĂNG LƯỢNG HOÀNG VIÊN**

Đ/C:XÃ LONG BÌNH, HUYỆN PHÚ RIỀNG, TỈNH BÌNH PHƯỚC

CHỦ TRÌ

QUẢN LÍ KĨ THUẬT

NGƯỜI VẼ

GIÁM SÁT THI CÔNG CHỦ ĐẦU TƯ

.....

GIAI ĐOẠN STAGE

BẢN VẼ HOÀN CÔNG

HẠNG MỤC CÔNG TRÌNH BUILDING ITEM

TÊN BẢN VẼ DRAWING TITLE

**SƠ ĐỒ NGUYÊN LÝ**

LẮP PIN NĂNG LƯỢNG MẶT TRỜI

| TỶ LỆ SCALE | NGÀY HOÀN THÀNH DATE | SỐ BẢN VẼ DRAWING NO. |
|---|---|---|
| ... | /2019 | |