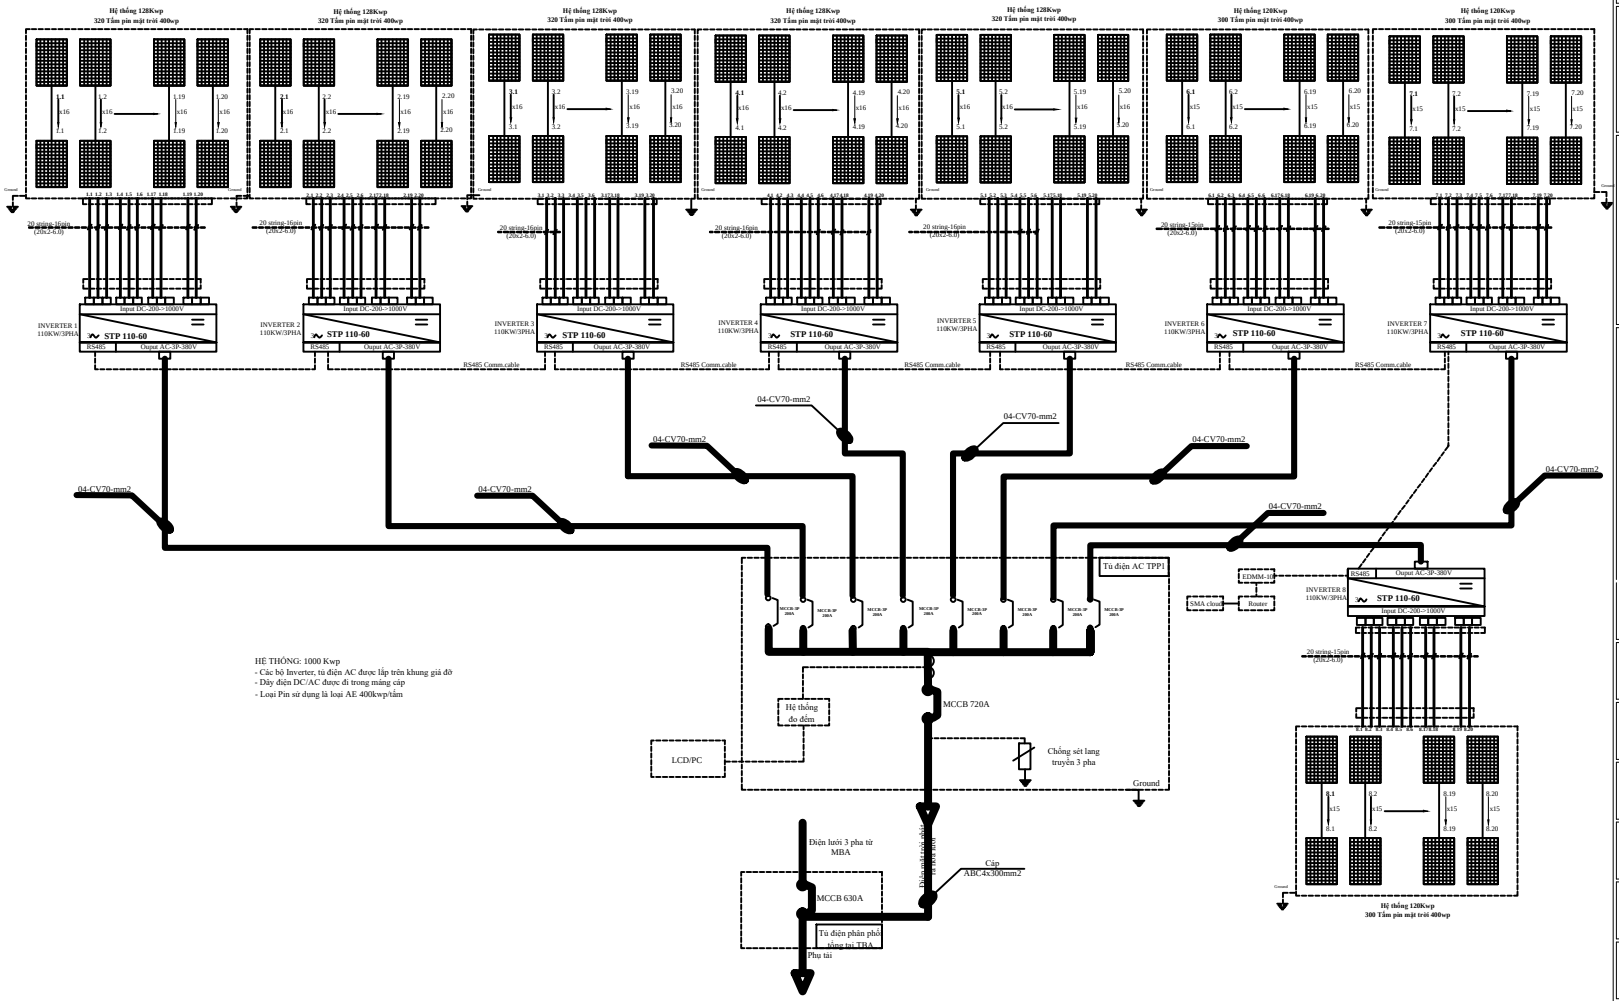


HIỆU CHỈNH			REVISION
STT NO	NGÀY DATE	NỘI DUNG DESCRIPTION	DUYỆT APPROVAL
1			
2			
3			

TÊN DỰ ÁN — PROJECT NAME

XÂY DỰNG HỆ THỐNG NLMTAM 1000 KWP CTY TNHH NÔNG NGHIỆP NĂNG LƯỢNG HOÀNG VIÊN

Đ/C: XÃ PHƯỚC MINH, HUYỆN BÙ GIA MẬP, TỈNH BÌNH PHƯỚC

CHỦ ĐẦU TƯ — OWNER

CÔNG TY TNHH NÔNG NGHIỆP NĂNG LƯỢNG HOÀNG VIÊN

Đ/C:XÃ PHƯỚC MINH, HUYỆN BÙ GIA MẬP, TỈNH BÌNH PHƯỚC

CHỦ TRÌ

QUẢN LÍ KĨ THUẬT

NGƯỜI VẼ

GIÁM SÁT THI CÔNG — CHỦ ĐẦU TƯ

.....

GIAI ĐOẠN — STAGE

BẢN VẼ HOÀN CÔNG

HẠNG MỤC CÔNG TRÌNH — BUILDING ITEM

TÊN BẢN VẼ — DRAWING TITLE

SƠ ĐỒ NGUYÊN LÝ

LẮP PIN NĂNG LƯỢNG MẶT TRỜI

TỶ LỆ SCALE	NGÀY HOÀN THÀNH DATE	SỐ BẢN VẼ DRAWING NO.
...	/2019	