

DỰ ÁN GIA HÂN BÌNH LONG 1,2MWp

[illegible][illegible]

HIỆU CHỈNH		REVISION	
STT	NGÀY	NỘI DUNG	DUYỆT
NO.	DATE	DESCRIPTION	APPROVAL
1			
2			
3			

TÊN DỰ ÁN

PROJECT NAME

NĂNG LƯỢNG MẶT TRỜI

ÁP MÁI 1200KW

ĐC: Xã Thanh An, huyện Bình Long, Tỉnh Bình Phước

CHỦ ĐẦU TƯ
OWNER
Cty TNHH Phước Thiện
Bình Phước
Đ/C: Ấp Mước Mắm, Xã Phước Thiện, Huyện Bình Phước
Độc, Tỉnh Bình Phước

ĐƠN VỊ THI CÔNG


HMT
HIỆP MINH THINH
SOLAR

**CTY TNHH HIỆP
MINH THINH**

ĐC: TT THANH BÌNH, HUYỆN BÚ ĐOP, TỈNH BÌNH PHƯỚC
ĐT: 08 6663 8667
EMAIL: HIEMINHTHINH@GMAIL.COM

GIAM ĐỐC	MA ĐỨC AN	CHỦ TRÌ	HUYỀN CAO TUYÊN	QUẢN LÝ THUẬT	NGUYỄN ĐÌNH PHÚ	NGƯỜI VỆ	HÀ LỊCH PHÚ	GIAM SÁT THỊ CÔNG	CHỦ ĐÀU TƯ
----------	-----------	---------	-----------------	---------------	-----------------	----------	-------------	-------------------	------------

STAGE	GIA ĐOÀN
BÀN VỀ HOÀN CÔNG	
BUILDING ITEM	HÀNG MỤC CÔNG TRÌNH
DRAWING TITLE	TÊN BẢN VẼ
BÀN VỀ MẶT BẰNG	

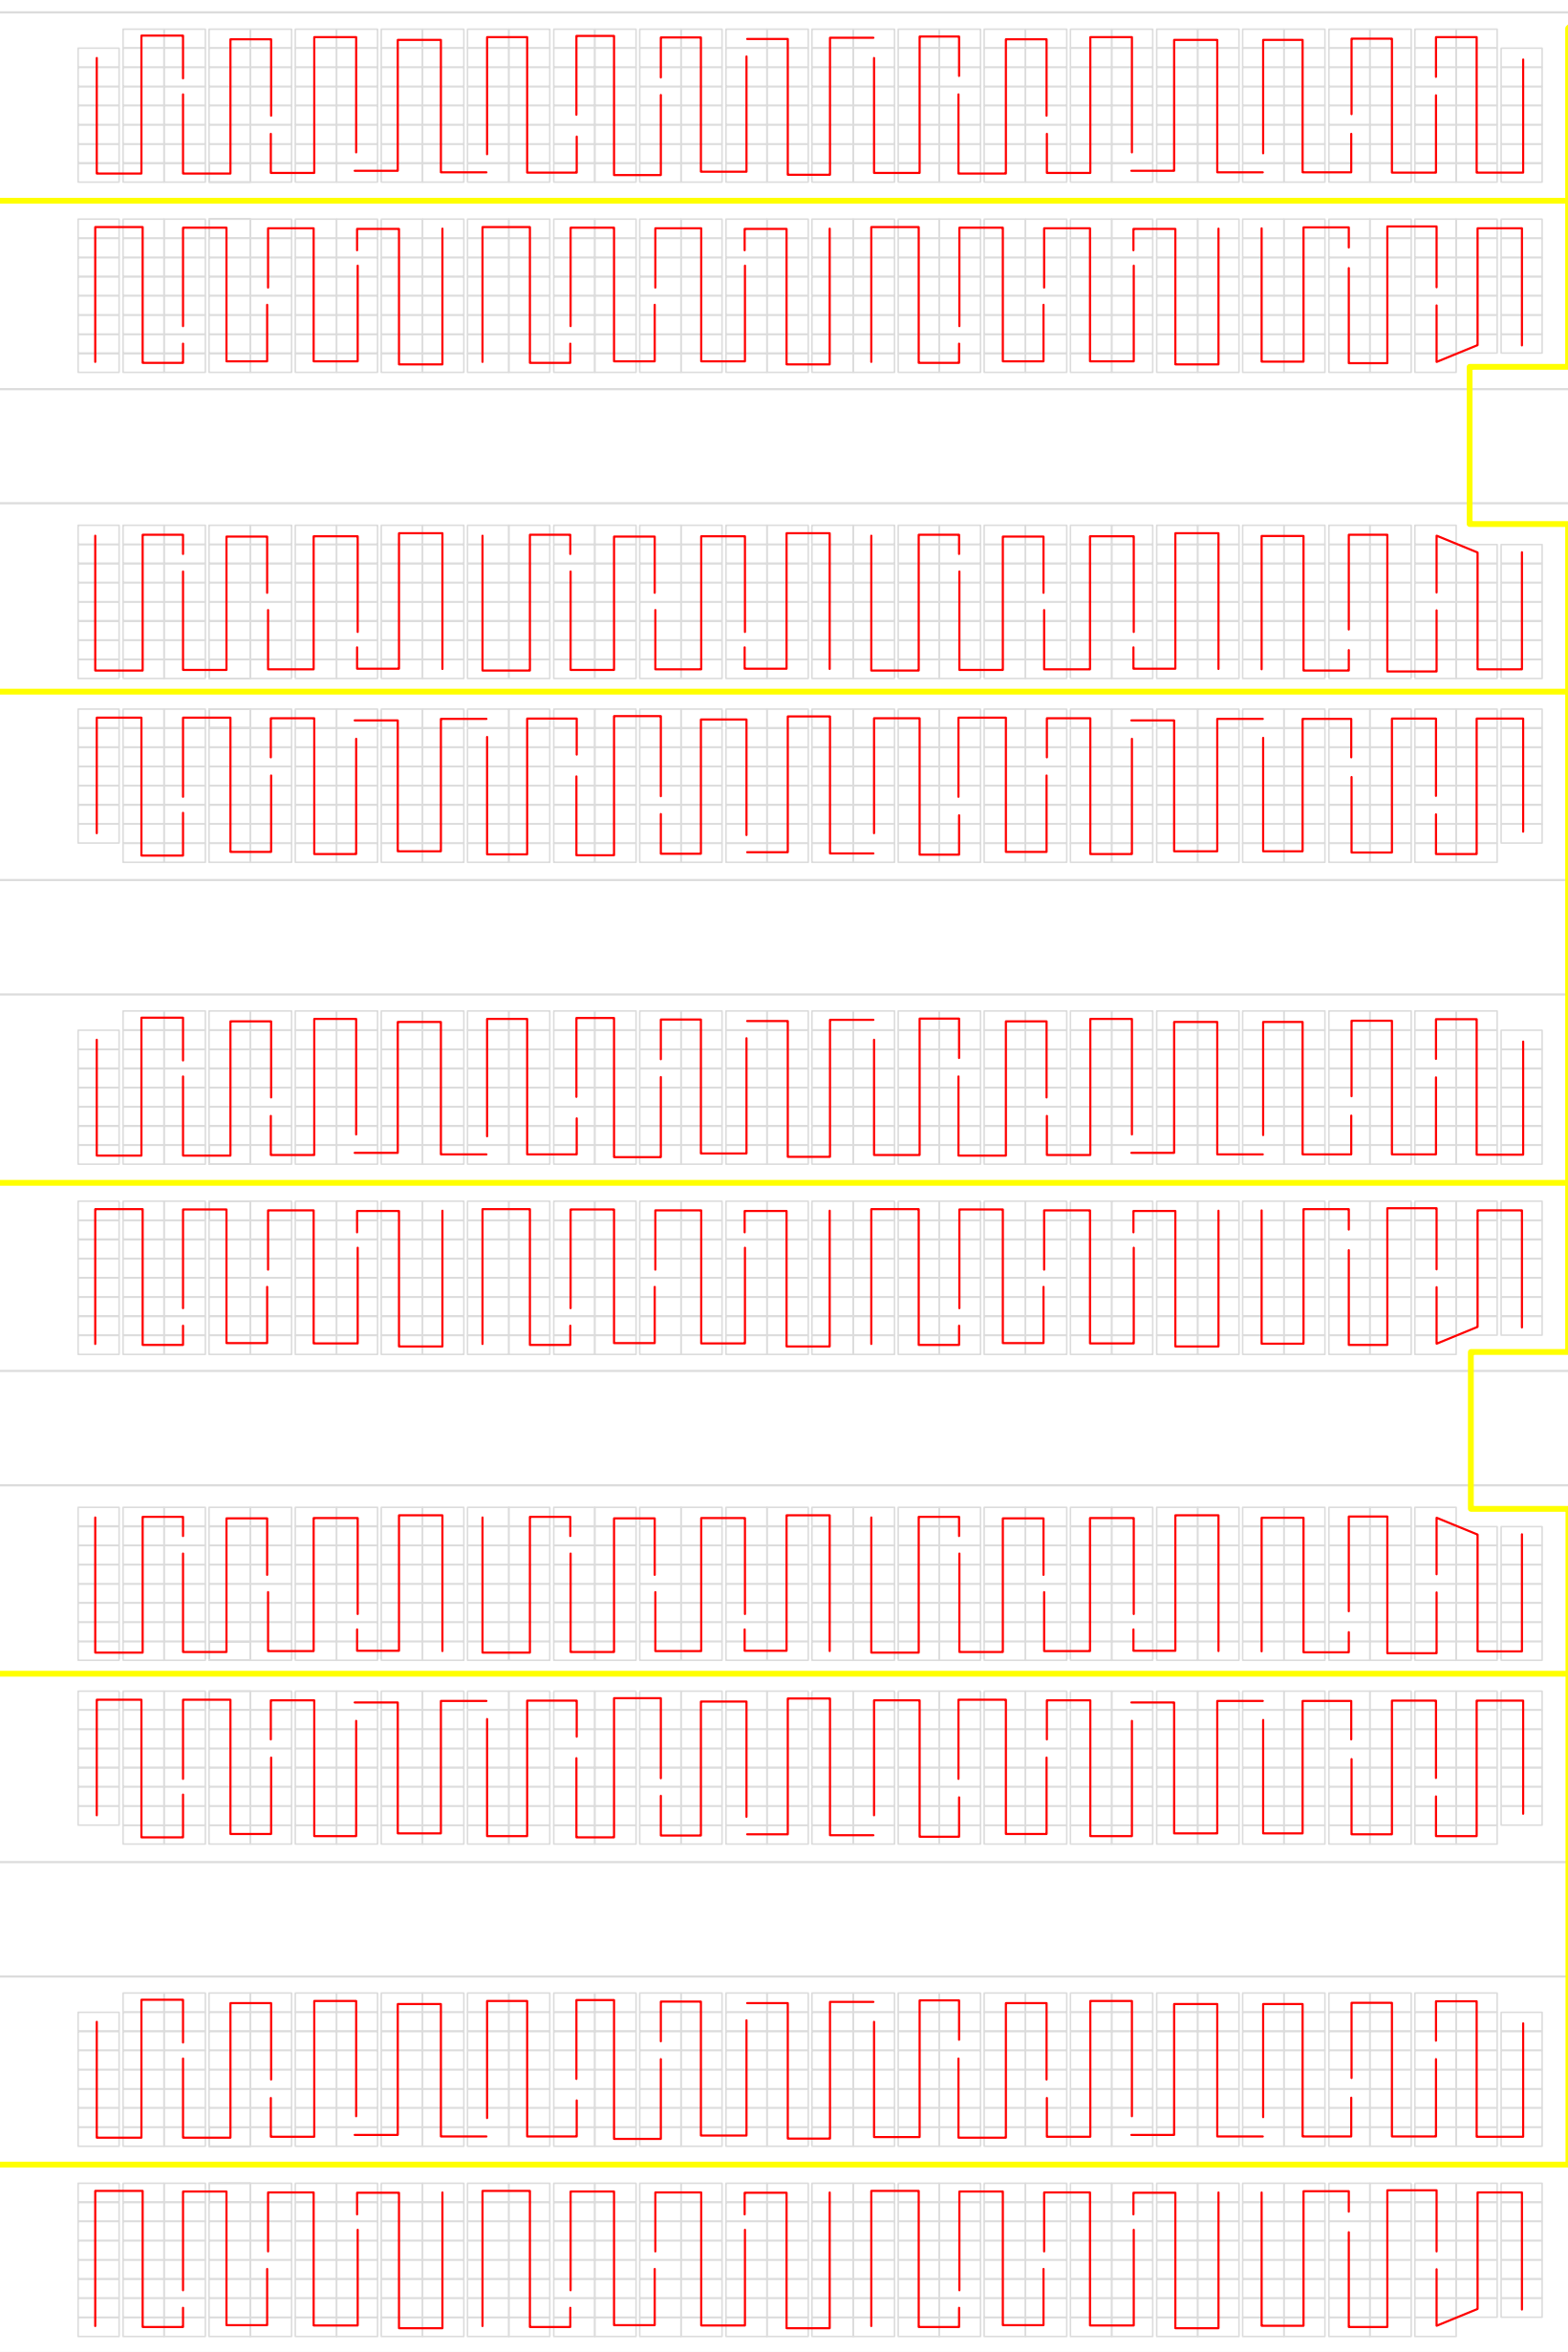

$2 * 15 * 18 \text{ string} = 445 * 15 * 18 * 2 = 240,$

$2 \times 15 \times 18 \text{ string} = 445 \times 15 \times 18 \times 2 = 240,3 \text{Kwp}$

$2 \times 15 \times 18 \text{ string} = 445 \times 15 \times 18 \times 2 = 240,3\text{K}_{wp}$

2*15*18 string=445*15*18*2=240,3Kwp

$2 \times 15 \times 18 \text{ string} = 445 \times 15 \times 18 \times 2 = 240,3 \text{Kwp}$

TỶ LỆ SCALE	NGÀY HOÀN THÀNH DATE	SỐ BẢN VẼ DRAWING NO.
	12/2024	