

HIỆU CHỈNH		REVISION	
STT	NGÀY	NỘI DUNG	DUYẾT
NO	DATE	DESCRIPTION	APPROVAL
1			
2			
3			

TÊN DỰ ÁN PROJECT NAME

NĂNG LƯỢNG MẶT TRỜI
ÁP MÁI

D/C.: XÃ THUẬN LỢI, HUYỆN ĐÔNG PHÚ,
TỈNH BÌNH PHƯỚC

CHỦ ĐẦU TƯ OWNER

CÔNG TY TNHH PHƯƠNG ANI

D/C.: XÃ THUẬN LỢI, HUYỆN ĐÔNG PHÚ,
TỈNH BÌNH PHƯỚC

ĐƠN VỊ THI CÔNG

HMT
HIỆP MINH THỊNH
SOLAR
CTY TNHH HIỆP
MINH THỊNH

D/C.: TT THANH BÌNH, HUYỆN BÙ ĐOP, TỈNH BÌNH PHƯỚC
ĐT.: 08.6683.6667
EMAIL: HIEMINHTHINH@GMAIL.COM

GIÁM ĐỐC

TRƯỞNG CÔNG TRÌNH

CHỦ TRÌ

HUYỆN CAO TOÀN

QUẬN LÃI THUẬT

NGUYỄN ĐÌNH PHI

NGƯỜI VẼ

HÀ LỊCH PHÚ

GIÁM SÁT THI CÔNG

GIAI ĐOẠN STAGE

BẢN VẼ THIẾT KẾ

HÀNG MỤC CÔNG TRÌNH

BUILDING ITEM


TÊN BẢN VẼ DRAWING TITLE

LẬP PİN NĂNG LƯỢNG MẶT TRỎ

TỶ LỆ	NGÀY HOÀN THÀNH	SỐ BẢN VẼ
SCALE	DATE	DRAWING NO.

... /2020

Phần nối ray (Nối 7 dãy ray mái 3
và 3 mái hướng nam còn lại)

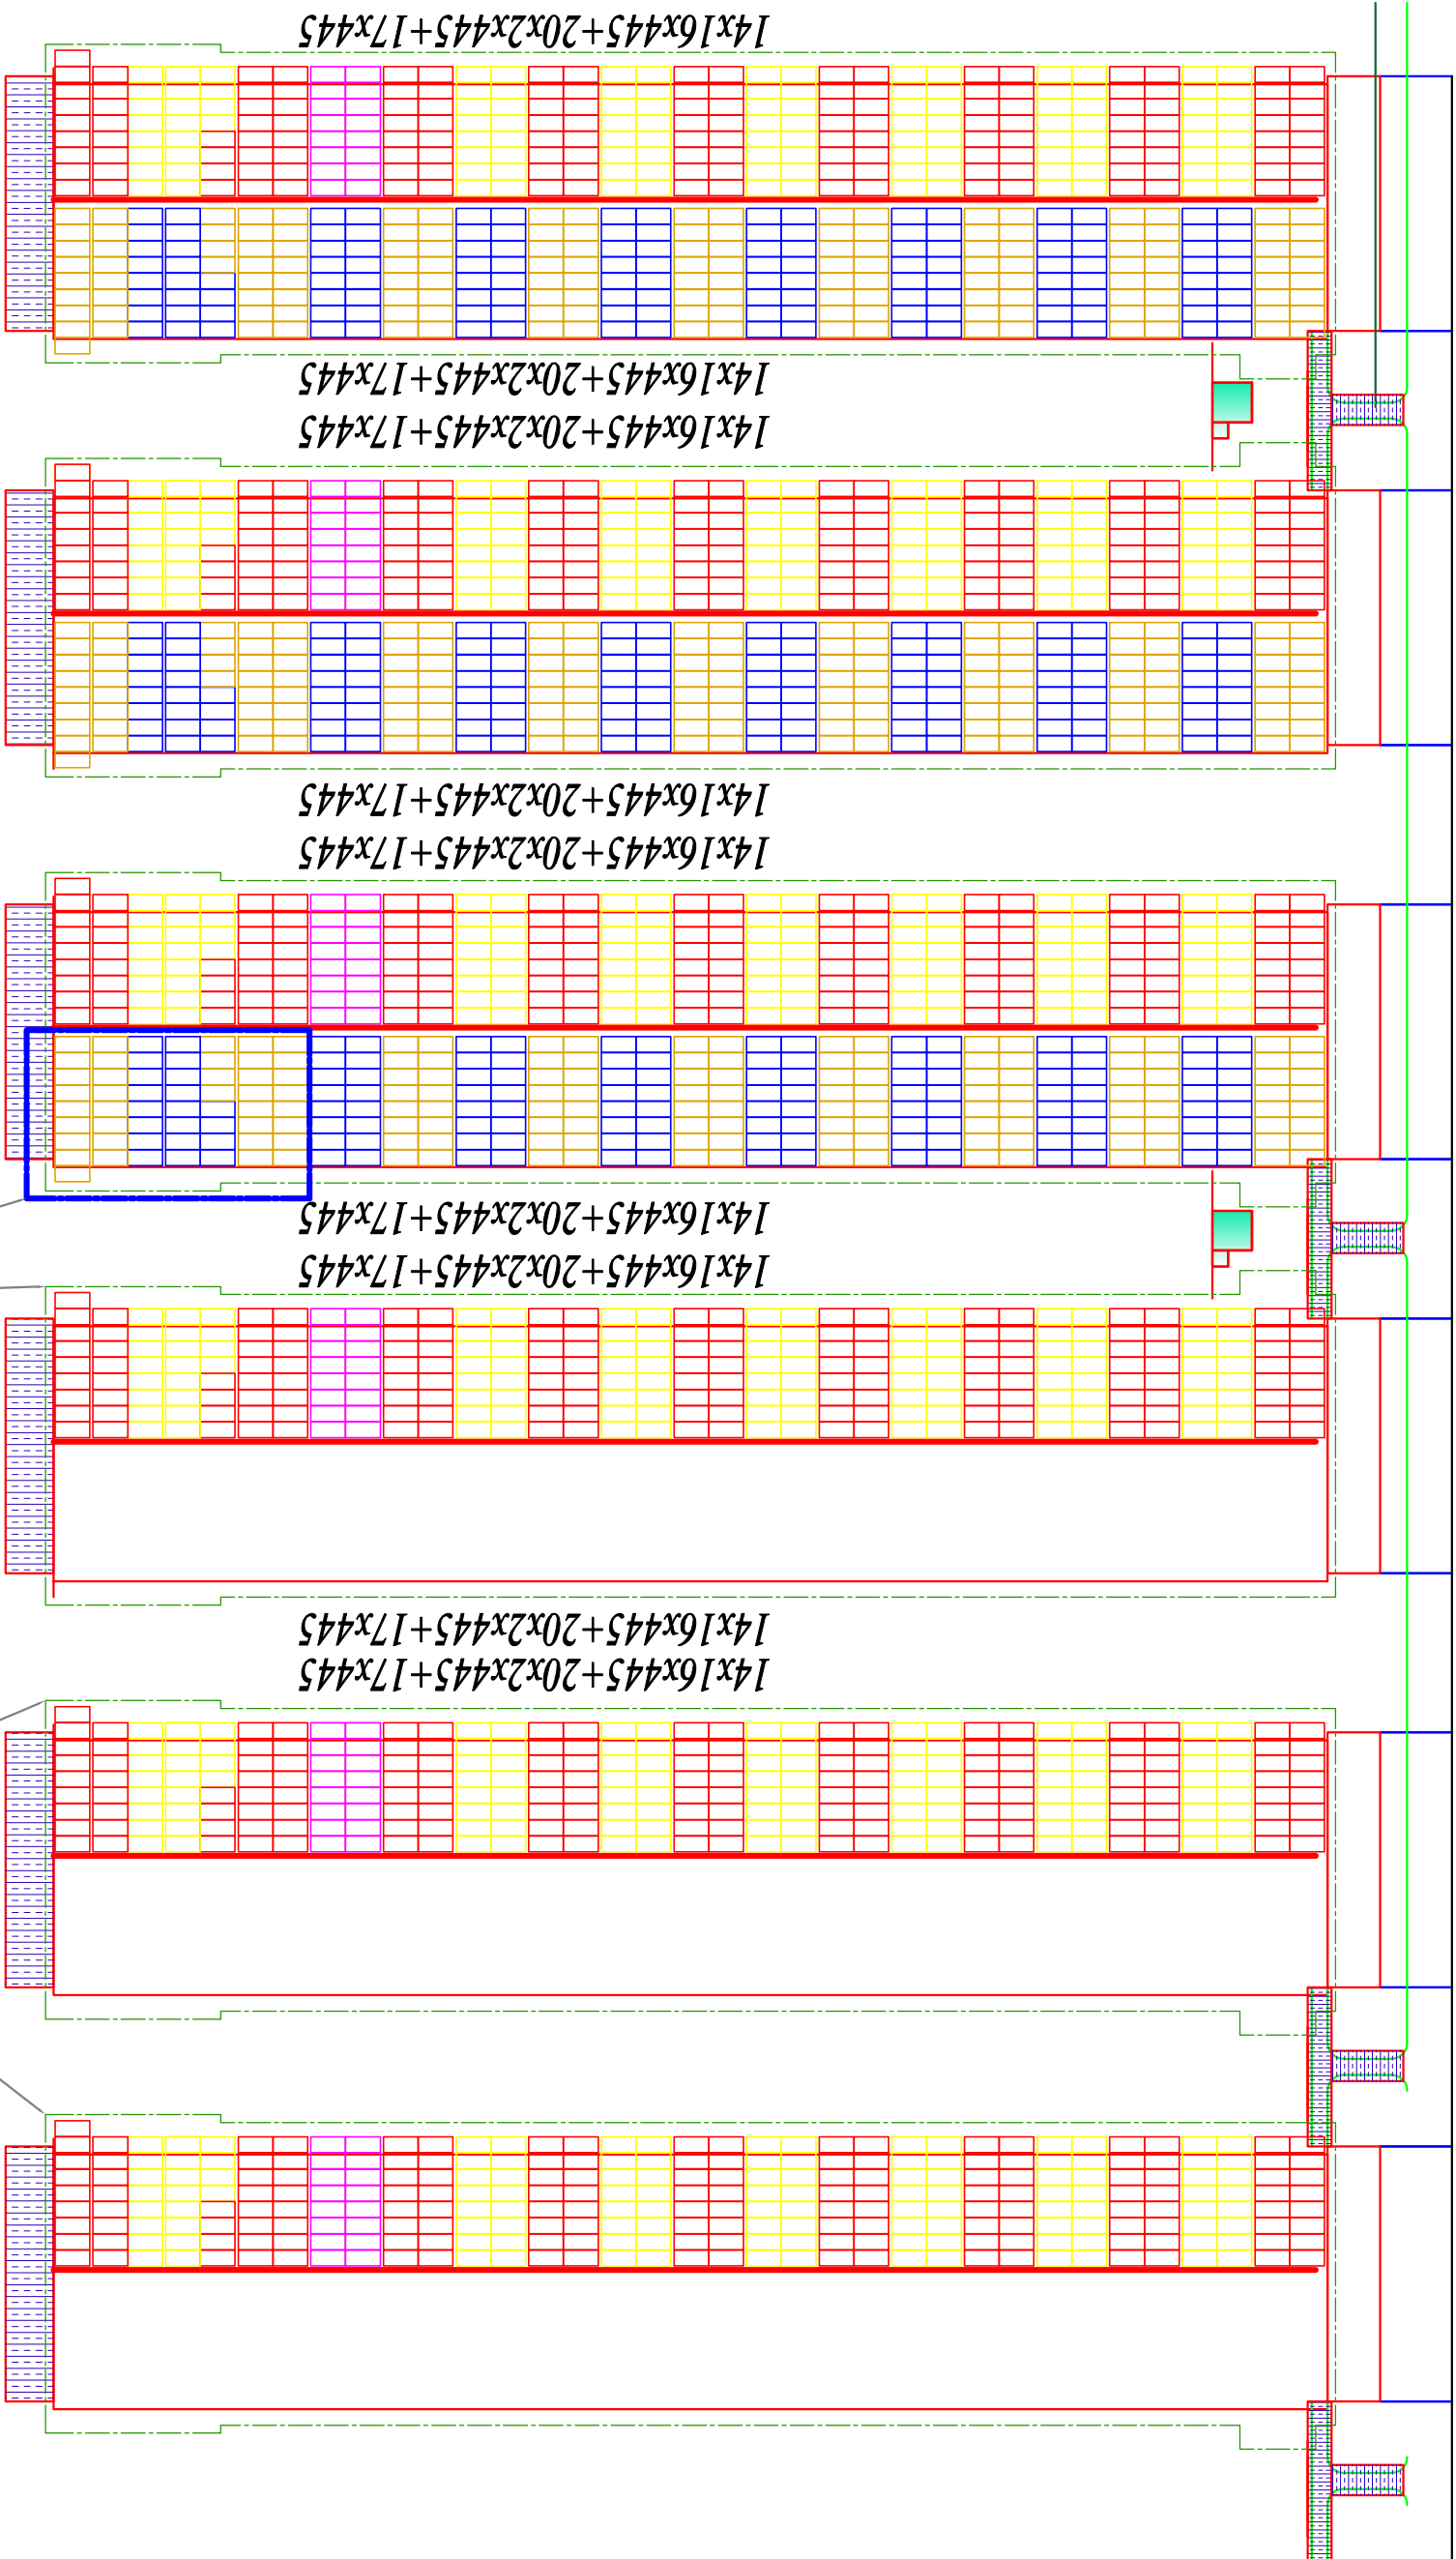

25



25



25



25



25



25