
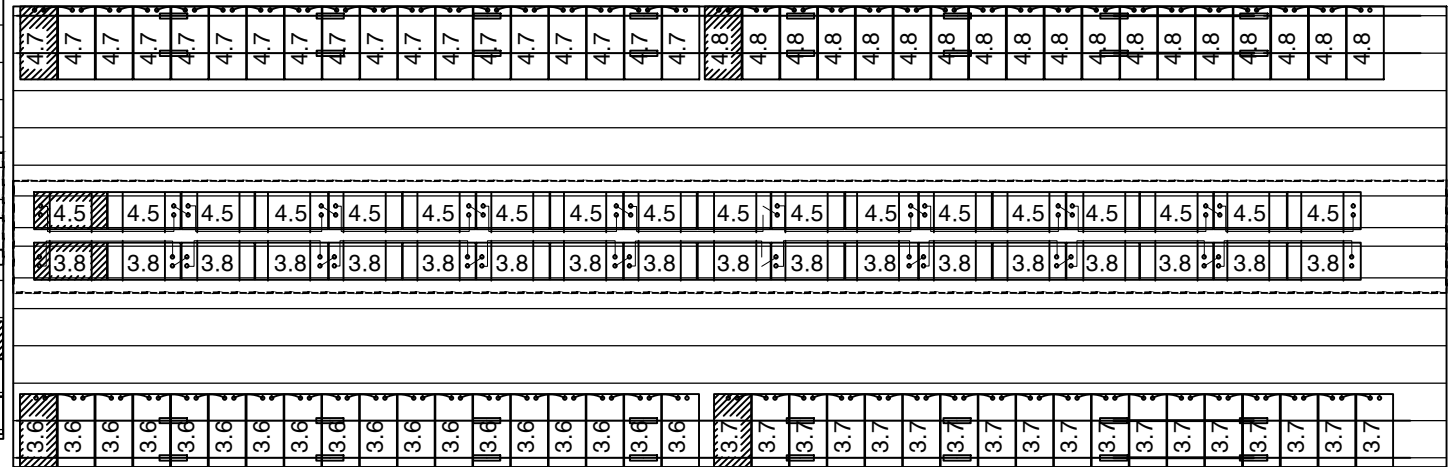
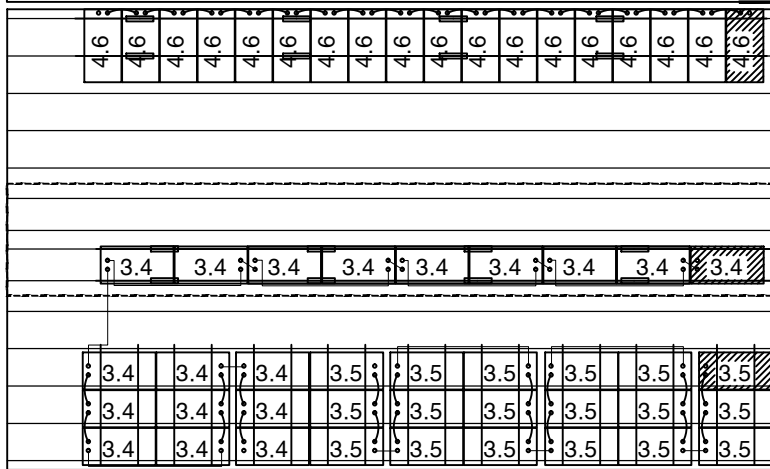
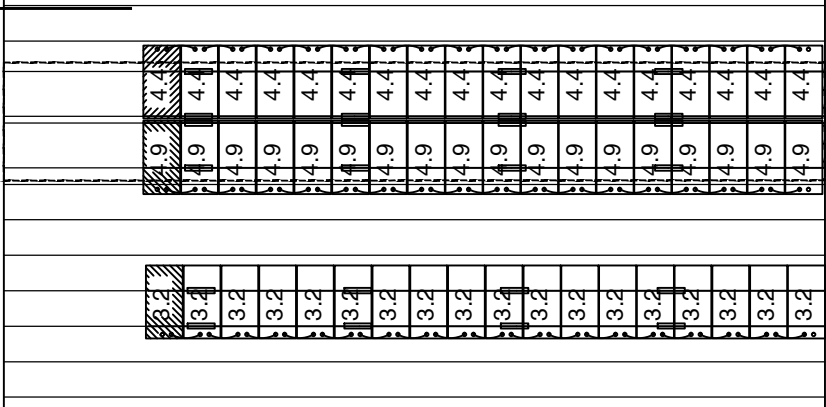
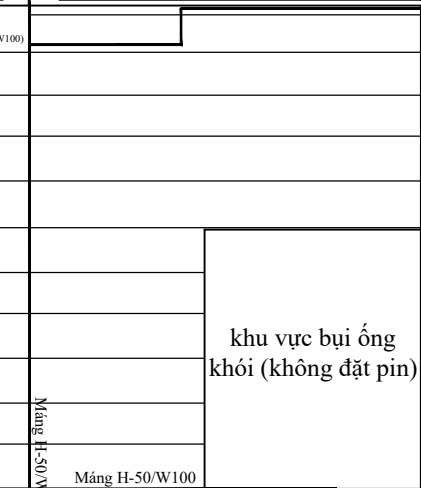
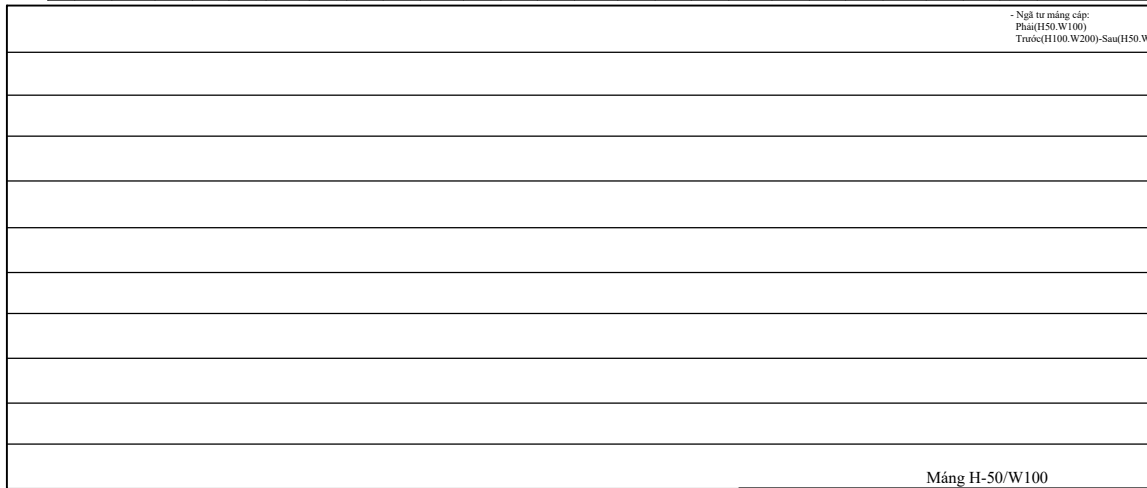
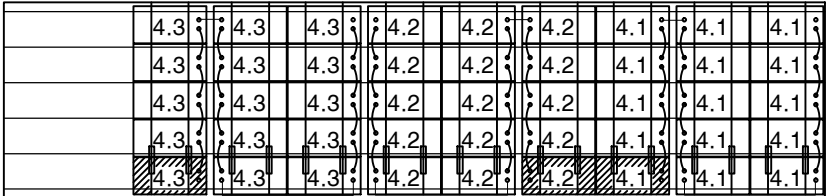
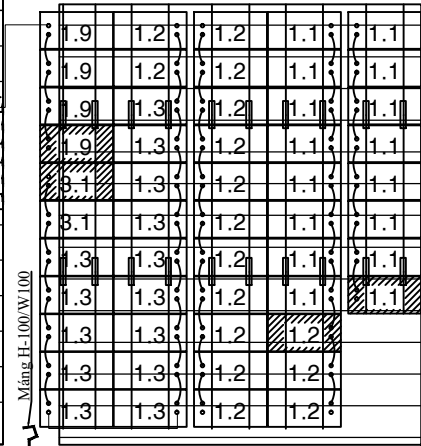


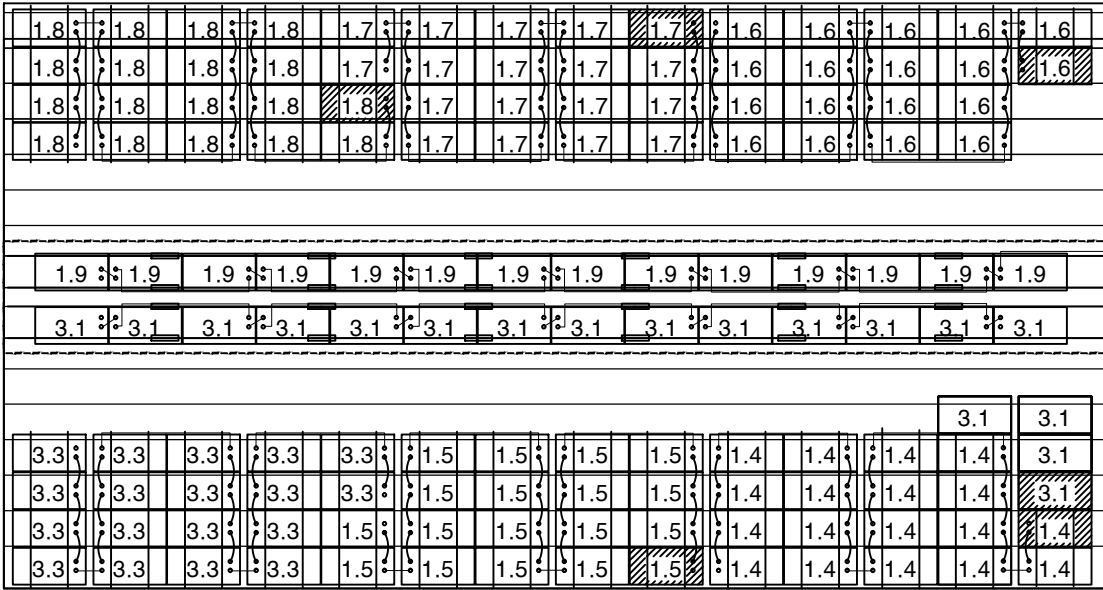

Tổng cộng: 167.61Kwp
- SL panel: 453 Tấm
- 20 String 18
- 3 string 16
- 3 string 15

Cường (57,72KWP)
invt 1: 50KW

16	18	18	18
16	18	18	18
16	..		

Hoa (109,89KWP)

invt 3: 50KW

18	18	18	18
18	18	18	18
..	..		

invt 4: 50KW

15	18	18	18
15	18	18	18
15	..		

MÁNG CÁP CHÍNH
-MÁNG CÁP: H100-W100-1.5-36m (Đã bao gồm nối máng)
-MÁNG CÁP: H50-W100-1.5-60m (Đã bao gồm nối máng)
-MÁNG CÁP: H100-W200-1.5-15m (Đã bao gồm nối máng)
PHỤ KIỆN MÁNG CÁP
- Tên ngang máng cáp:
Trái(H50.W100)-giữa(H50.W100)-phải(H50.W100): SL=01
- Co ngang máng cáp: H100.W200: SL=01
- Ngã tư máng cáp:
Trái(H100.W100)-phải(H50.W100)
Trước(H100.W200)-Sau(H50.W100): SL=01
- Co xuống máng cáp: H100.W200: SL=03
- Co lên máng cáp: H100.W200: SL=03
- Ống nhựa HDPE F20: 250m

CÔNG TY TNHH HIỆP MINH THỊNH

Giám đốc	Trương Duy Thanh	
CNĐA	Huỳnh Cao Toàn	
Vẽ	Nguyễn Đình Phi	

CÔNG TRÌNH: HỆ THỐNG NLMTAM TẠI TRUNG TÂM THƯƠNG MẠI
ĐỊA ĐIỂM: TT THANH BÌNH - HUYỆN BÙ ĐÓP- TỈNH BÌNH PHƯỚC

Sơ đồ đấu dây & Máng cáp

T.K.K.T.C.T	Ngày	SĐDD-MC	Số BV	01
Tỉ lệ:	04/2020			01