


PHẦN BỐ CÔNG-SUẤT HMT
(PIN AE-400WP)

INVERTER	C/S (WP)	STRING	SỐ TẤM
INV_01	123.200	(14*20+14*2)*400	274
INV_02	127.200	(15*20)*400+16*450	283
INV_03	123.200	(13*20+2*18)*400	274
INV_04	124.800	(14*20+18*2)*400	277
Tổng	498.400		1.108

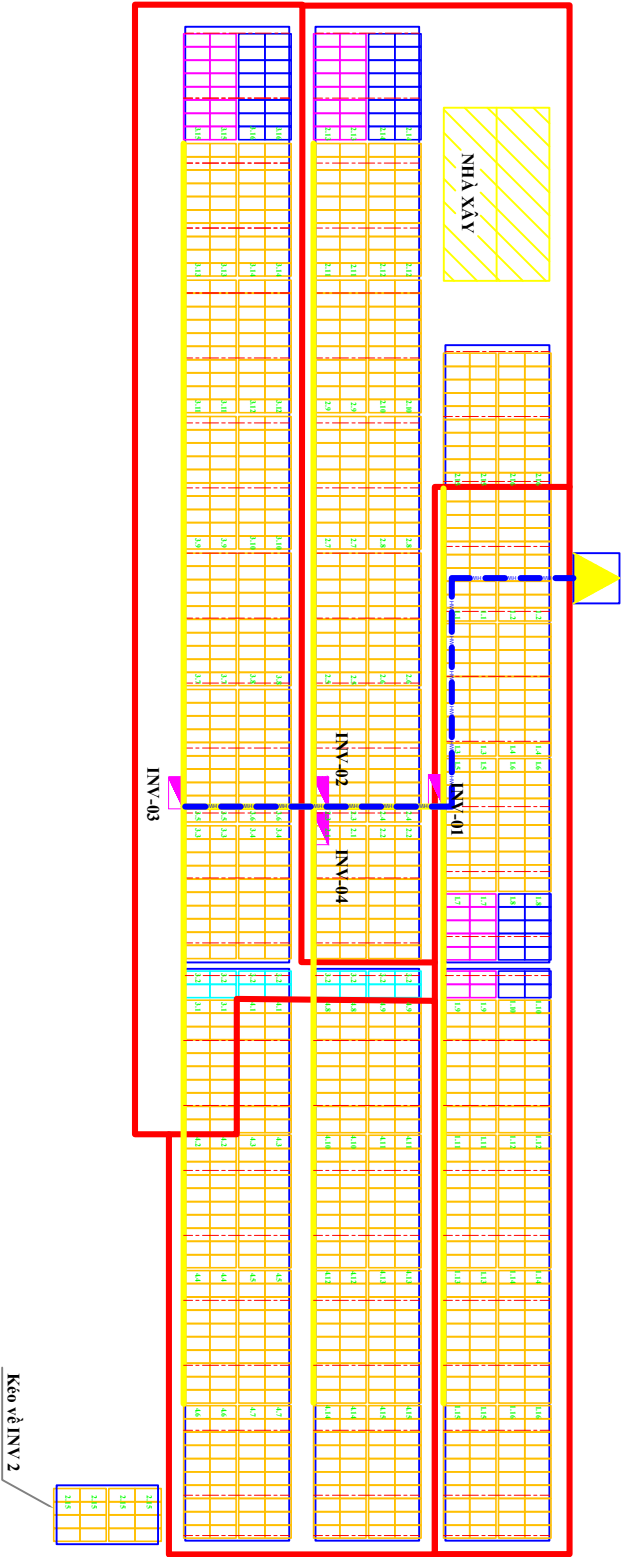

THIẾT KẾ		THIẾT KẾ	
STT	NGÀY	NỘI DUNG	ĐƯỢC
NO	DATE	DESCRIPTION	APPROVAL
1			
2			
3			

TÊN DỰ ÁN PROJECT NAME

NĂNG LƯỢNG MẶT TRỜI
CÔNG NGHỆ CAO

ĐC: Xã Lạc Ninh, Huyện Lạc Ninh, Tỉnh Bình Phước

CHỦ ĐẦU TƯ OWNER

CÔNG TY TNHH HIỆP MINH THỊNH

ĐC: TT THANH BÌNH, HUYỆN BÚ ĐOAN, TỈNH BÌNH PHƯỚC

ĐƠN VỊ THI CÔNG

HMT
HIỆP MINH THỊNH
SO LAR
CÔNG TY TNHH HIỆP MINH THỊNH

ĐC: TT THANH BÌNH, HUYỆN BÚ ĐOAN, TỈNH BÌNH PHƯỚC
ĐT: 08 6663 8667
EMAIL: HIEMINHTRUONG@GMAIL.COM

GIẤY ĐÓNG

TRƯỜNG CÔNG NGHỆ

CHẤT TR

HIỆP MINH THỊNH

QUẢN LÝ THI CÔNG

NGUYỄN DINH PHU

NGƯỜI VẼ

ĐẠI LỊCH PHU

GIẤY SẴN THI CÔNG

GAĐỒN

BẢN VẼ HOÀN CÔNG

HÀNG MỤC CÔNG TRÌNH

BUILDING TYPE

TÊN BẢN VẼ		DRAWING TITLE	
MẶT BẰNG TỔNG THỂ		GENERAL LAYOUT	
LẬP PIN NĂNG LƯỢNG MẶT TRỜI		SOLAR PANEL LAYOUT	
TỶ LỆ	KÝ HIỆU BẢN VẼ	SỐ BẢN VẼ	ĐIỀU KIỆN
SCALE	DATE	DRAWING NO.	CONDITION
1:1000	2020	KC - 00	