


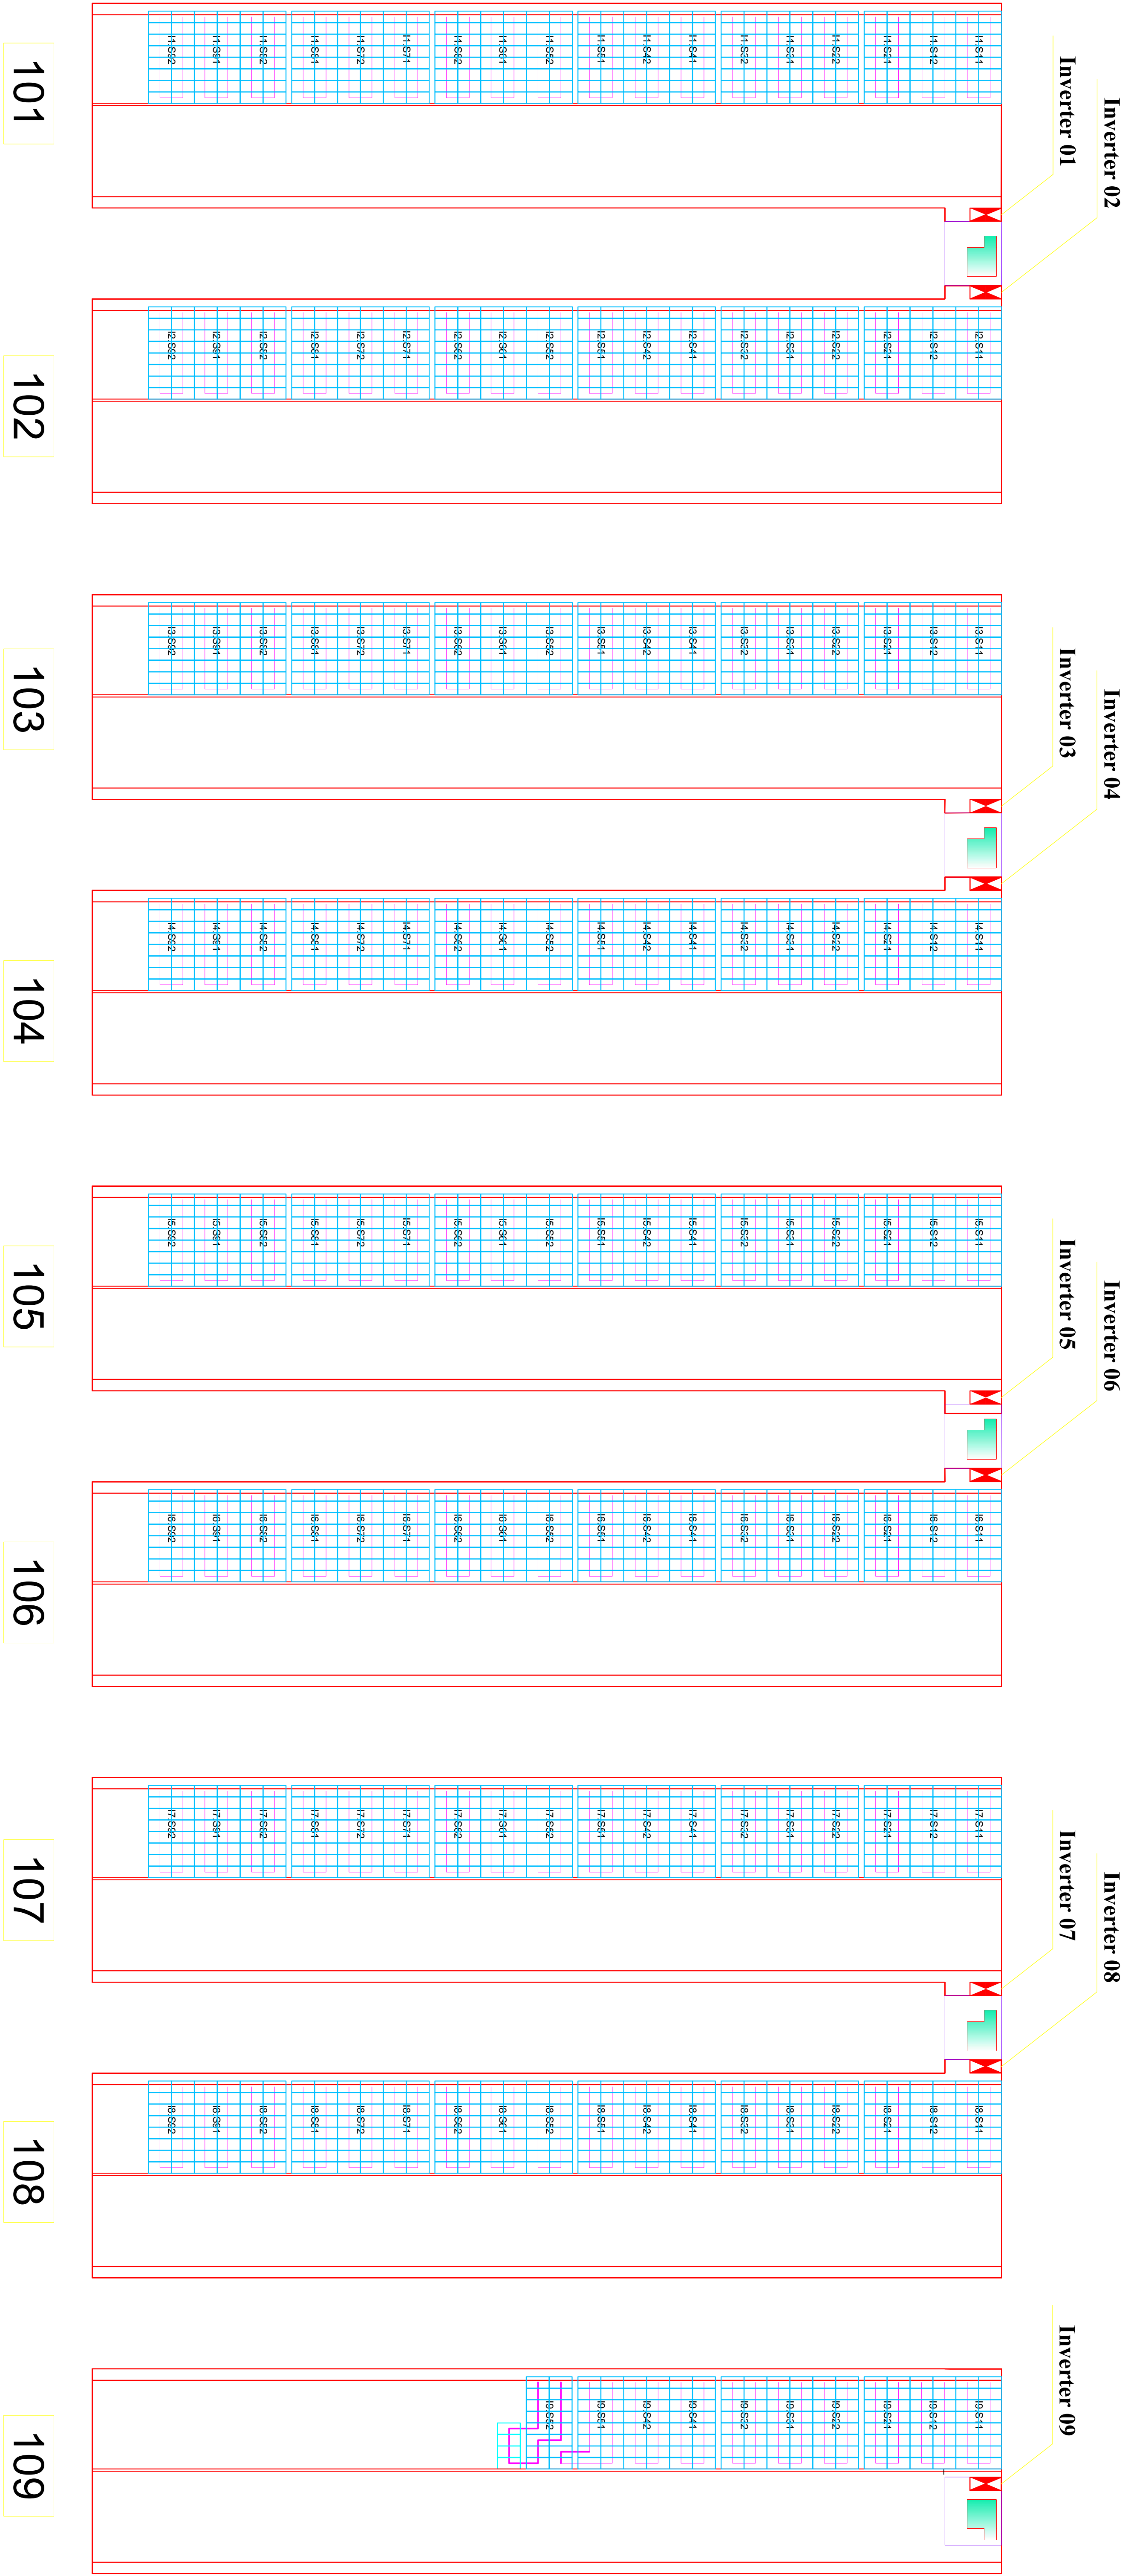

SƠ ĐỒ ĐẦU NỐI STRING ĐẾN INVERTER

BỐ TRÍ TẮM PIN NĂNG LƯỢNG MẶT TRỜI JAM405					
TT	TÊN CHUỖNG	SỐ LƯỢNG TẮM PIN (TẮM)	CÔNG SUẤT TẮM PIN (KWP)	CÔNG SUẤT INVERTER (KW)	ĐIỂM ĐẦU NỐI
1	101	288	116.640	110	Trạm biến áp số 1 - 560KVA
2	102	288	116.640	110	Trạm biến áp số 1 - 560KVA
3	103	288	116.640	110	Trạm biến áp số 1 - 560KVA
4	104	288	116.640	110	Trạm biến áp số 1 - 560KVA
5	105	288	116.640	110	Trạm biến áp số 1 - 560KVA
6	106	288	116.640	110	Trạm biến áp hiện hữu - 400KVA
7	107	288	116.640	110	Trạm biến áp hiện hữu - 400KVA
8	108	288	116.640	110	Trạm biến áp hiện hữu - 400KVA
9	109	164	66.420	50	Trạm biến áp hiện hữu - 400KVA
TỔNG CỘNG		2468	999.540	930	

I2.S11

S: String/ 11: MPPT01 & Track 01

I: Inverter/ 2: Number of Inverter

TI lệ - Scale	BẢN VẼ SỐ
1:	Drawing No.
Tháng - Month	
....../2020	

TÊN DỰ/AN
(Project Name)

TÊN DỰ/AN: LẬP DÂY HỆ THỐNG ĐIỆN MẶT TRỜI ÁP MẶT TRÊN MÀI TRẢI HỒ

ĐỊA ĐIỂM XÂY DỰNG
(Site)

Xã Phước Thới, huyện Bì Động, tỉnh Bình Phước

CHỦ ĐẦU TƯ
(Project Owner)

CÔNG TY TNHH CHẨN NỘI

LỘC THIỆN

GIÁM ĐỐC

NHÀ THẦU
(Contractor)

CÔNG TY CỔ PHẦN CƠ BIẾN

CTH

BỘ CÔNG SỞ HƯỚNG TRƯỜNG PHƯỚC CHƠN

TRƯỜNG CÔNG TRÌNH THIÊN PHƯỚC

P: GIÁM ĐỐC

ĐÀO TRẦN VINH QUỐC

CHỦ HUY TRƯỞNG

KS. LÊ TRỌNG NHẬN

GIÁM SÁT LỄ TRỌNG NHẬN

GIÁM SÁT NGƯỜI MÃI TÍNH

TÊN BẢN VẼ
(Drawing Title)