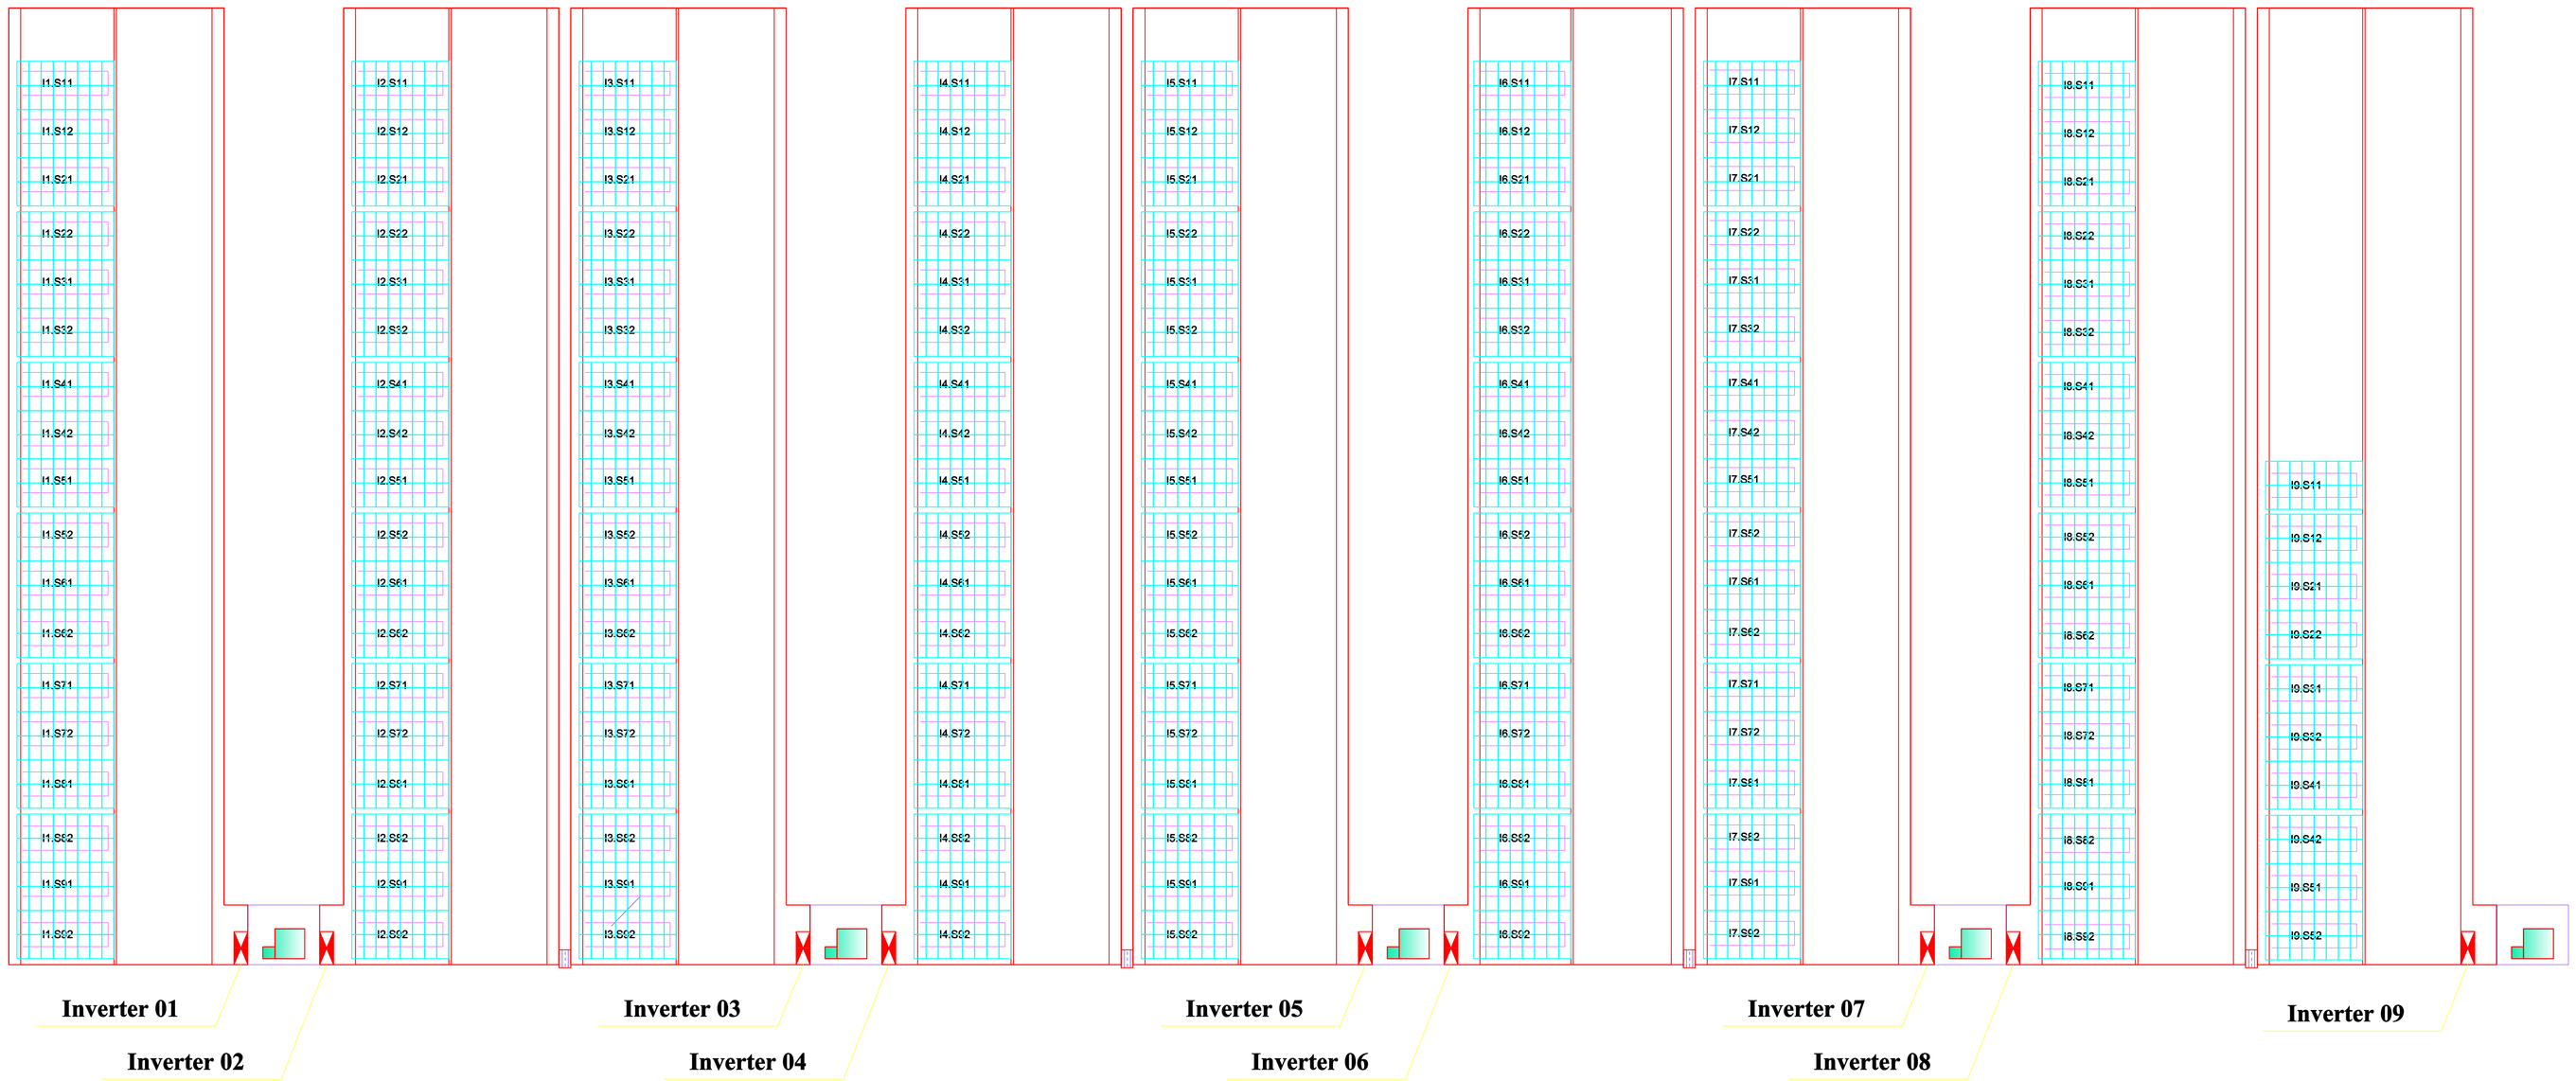


SƠ ĐỒ ĐẤU NỐI STRING ĐẾN INVERTER

BỐ TRÍ TẤM PIN NĂNG LƯỢNG MẶT TRỜI JAM405					
TT	TÊN CHUỖNG	SỐ LƯỢNG TẤM PIN (TẤM)	CÔNG SUẤT TẤM PIN (KWP)	CÔNG SUẤT INVERTER (KW)	ĐIỂM ĐẤU NỐI
1	201	288	116.64	110	Trạm biến áp số 2 - 1000kVA
2	202	288	116.64	110	Trạm biến áp số 2 - 1000kVA
3	202	288	116.64	110	Trạm biến áp số 2 - 1000kVA
4	202	288	116.64	110	Trạm biến áp số 2 - 1000kVA
5	202	288	116.64	110	Trạm biến áp số 2 - 1000kVA
6	202	288	116.64	110	Trạm biến áp số 2 - 1000kVA
7	202	288	116.64	110	Trạm biến áp số 2 - 1000kVA
8	202	288	116.64	110	Trạm biến áp số 2 - 1000kVA
9	202	160	64.80	50	Trạm biến áp số 2 - 1000kVA
TỔNG CỘNG		**2,464**	**997.92**	**930**	

I2.S11 S: String/ 11: MPPT01 & Track 01

I: Inverter/ 2: Number of Inverter

TÊN DỰ ÁN
(Project Name)

TÊN DỰ ÁN : LẮP ĐẶT HỆ THỐNG ĐIỆN NĂNG LƯỢNG MẶT TRỜI ÁP MÁI TRANG TRẠI CHĂN NUÔI HEO HẬU BỊ

ĐỊA ĐIỂM XÂY DỰNG
(Site)

Xã Phước Thiện, huyện Bù Đốp, tỉnh Bình Phước

CHỦ ĐẦU TƯ
(Project Owner)

CÔNG TY TNHH MTV NL NAM NHẬT

NHÀ THẦU
(Contractor)

CÔNG TY CỔ PHẦN CƠ ĐIỆN C T H

ĐỊA CHỈ: 941 HÙNG VƯƠNG, PHƯỜNG NHƠN PHÚ, TP QUY NHƠN, TỈNH BÌNH ĐỊNH

GIÁM ĐỐC

CHỦ TRÌ THIẾT KẾ

KS. LÊ TRỌNG NHÂN

KIỂM TRA	ĐÀO TRẦN VĨNH QUỐC	
THIẾT KẾ	LÊ TRỌNG NHÂN	

TÊN BẢN VẼ
(Drawing Title)

Tỉ lệ - Scale
1:

BẢN VẼ SỐ
Drawing No.

Tháng - Month
..../20....